



LANDSCAPE LEGEND			
SOFTSCAPE	TAG	QTY	HARDSCAPE
ORNAMENTAL GRASS	XX	XX	PROPOSED BUILDING
PERENNIAL	XX	XX	PARKING ZONE
SHRUB	XX	XX	2' x 2' SAW-CUT CONCRETE
DECIDUOUS TREE	XX	XX	2' x 4' SAW-CUT CONCRETE
ASPEN TREE	XX	XX	WALKWAY DOWNLIGHT
			3" SITE WALL / CURB

ARCHITECTURAL LANDSCAPE PLAN 1
1" = 10'-0"

CCY ARCHITECTS
VOO DOO AFFORDABLE HOUSING
TELLURIDE, COLORADO


DATE: 02 | 28 | 2022
ISSUE: PRELIMINARY HARC
PROJECT NUMBER: 21121
DRAWN BY: -- CHECKED BY: --

HISTORY:		
REV. #	DATE	DESCRIPTION

LANDSCAPE PLAN
SCALE: As indicated

A1.02



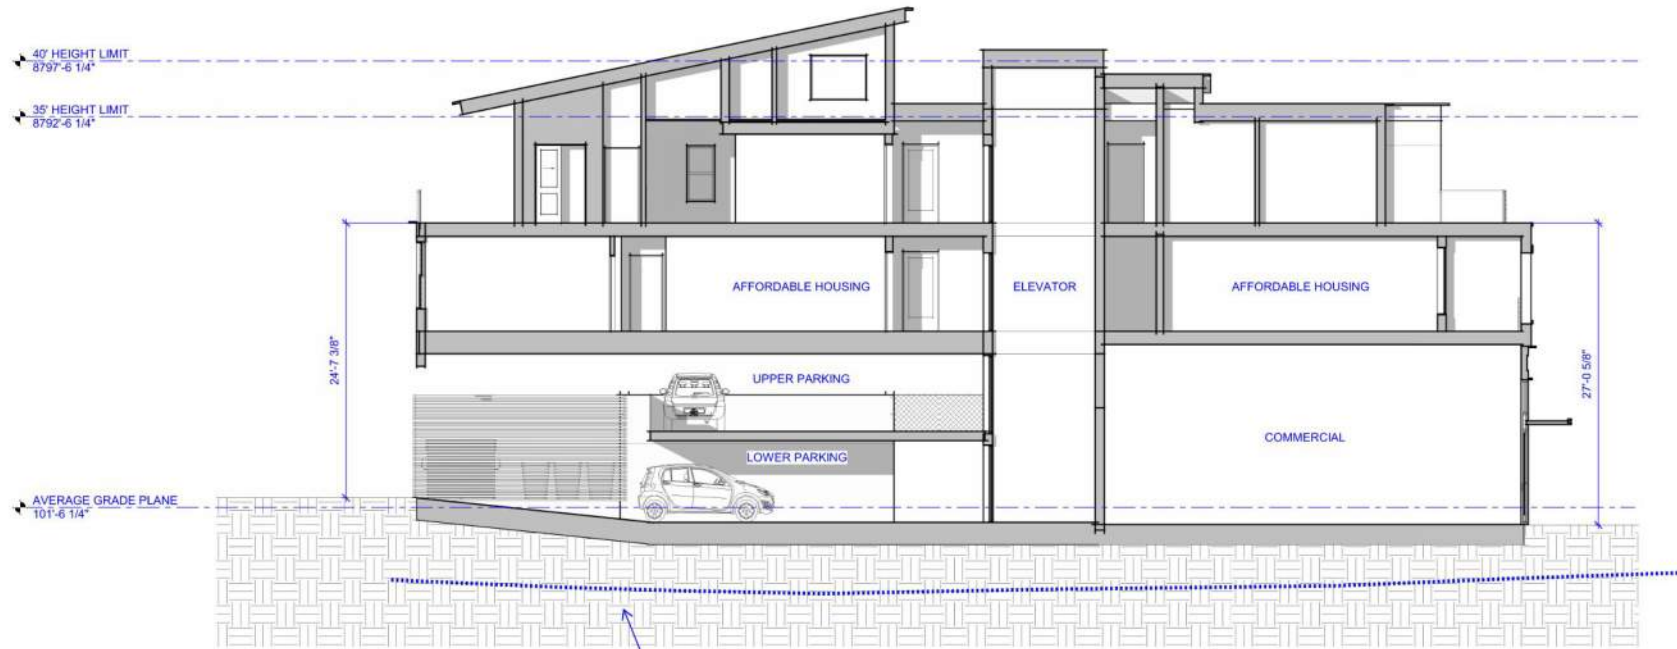

APPROXIMATE LINE OF
WATER TABLE

NORTH SOUTH SECTION - HARC
1/8" = 1'-0"

- 01 BRICK VENEER
- 02 METAL SIDING
- 03 WOOD SIDING
- 04 SLAT WALL
- 05 METAL ROOF

