
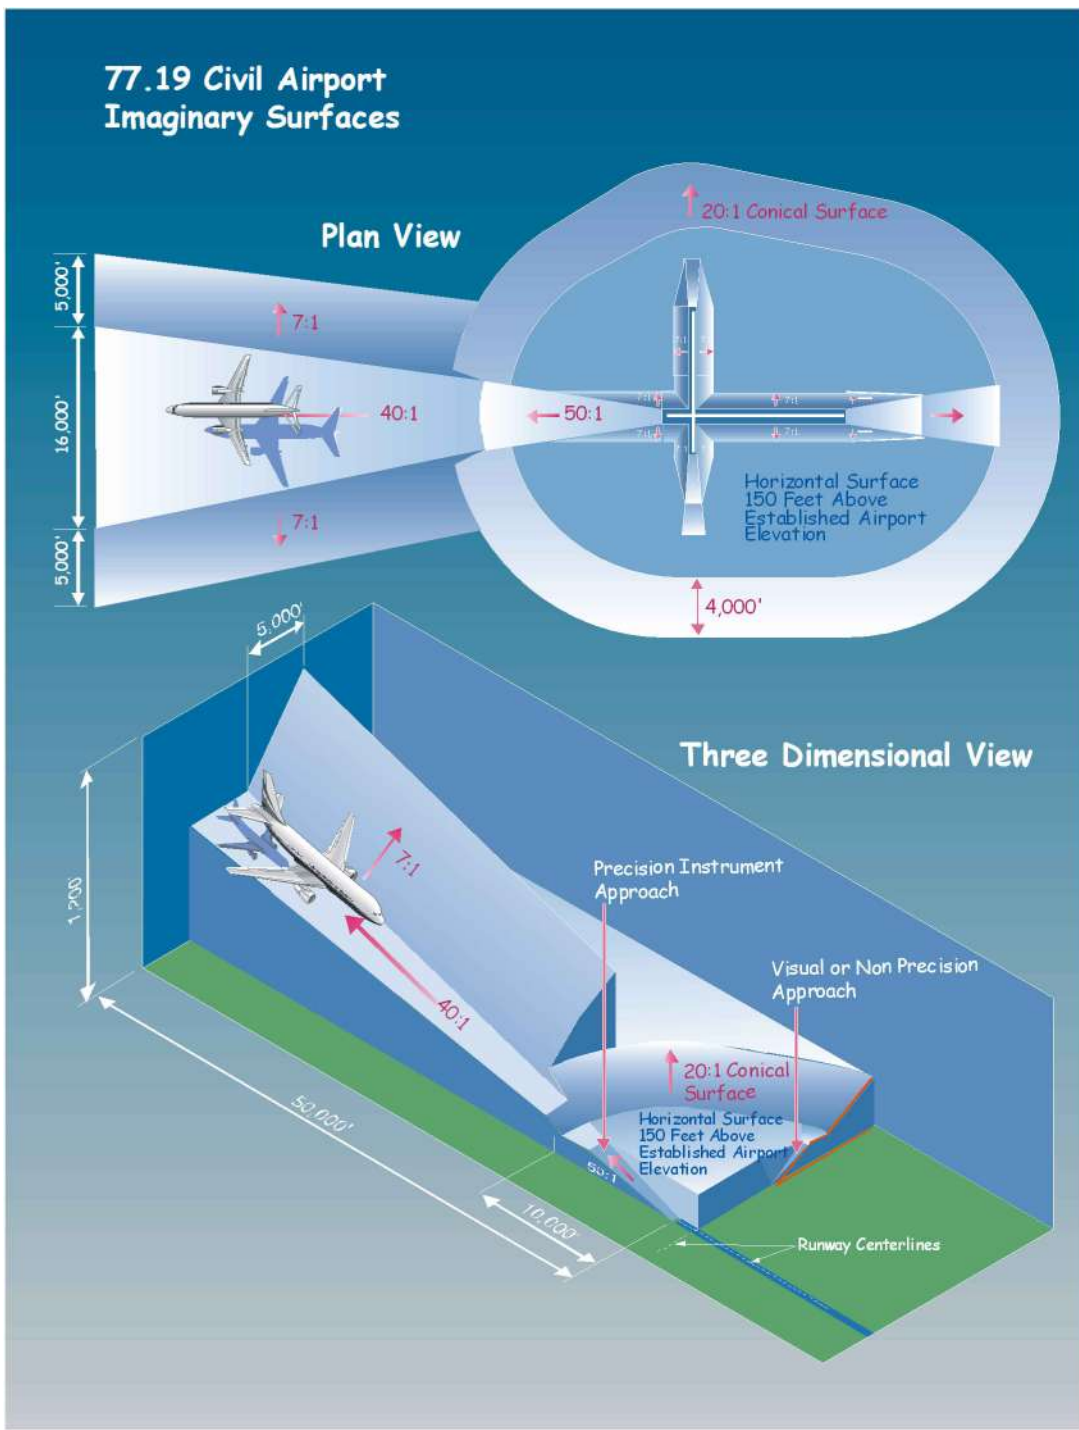


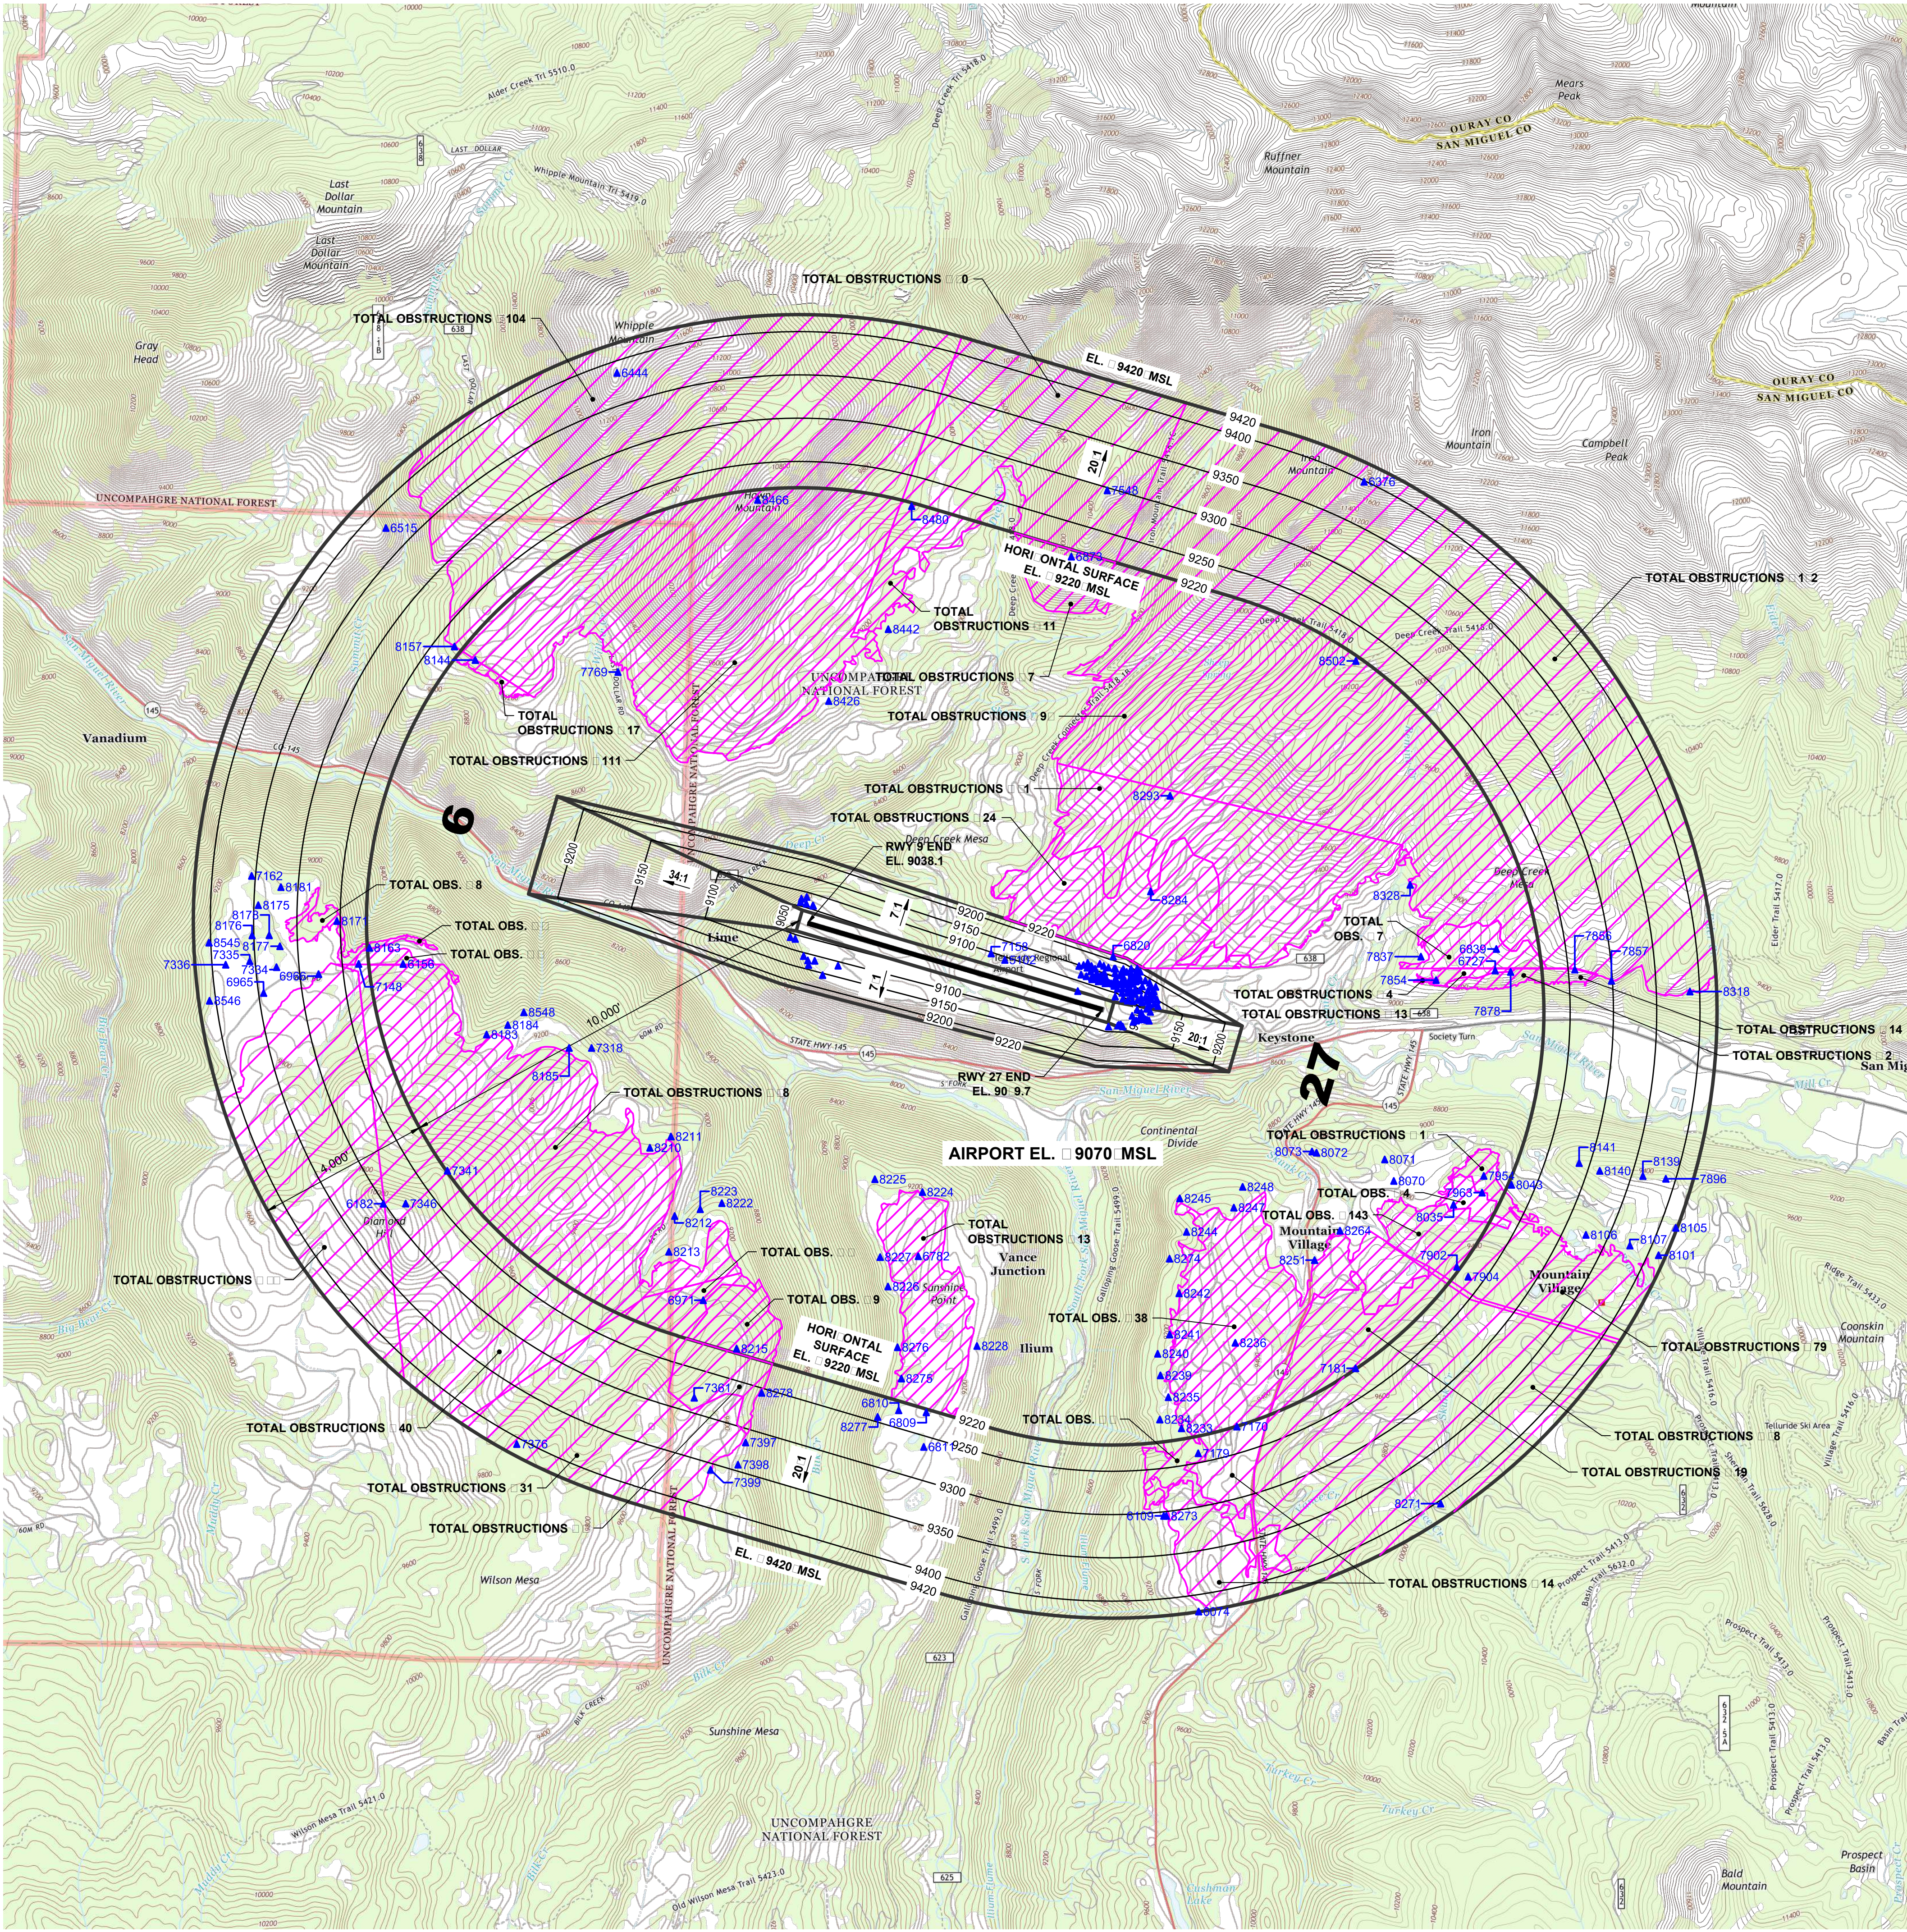


DIM	ITEM	DIMENSIONAL STANDARDS - FEET					
		VISUAL RUNWAY		NON-PRECISION INSTRUMENT RUNWAY		PRECISION INSTRUMENT RUNWAY	
		A	B	A	B	C	D
A	WIDTH OF PRIMARY SURFACE AND APPROACH SURFACE AT INNER END	250	500	500	500	1,000	1,000
B	RADIUS OF HORIZONTAL SURFACE	5,000	5,000	5,000	10,000	10,000	10,000
C	APPROACH SURFACE WIDTH AT END	VISUAL APPROACH		NON-PRECISION INSTRUMENT APPROACH		PRECISION INSTRUMENT APPROACH	
		A	B	A	B	C	D
C	APPROACH SURFACE WIDTH AT END	1,250	1,500	2,000	3,500	4,000	16,000
D	APPROACH SURFACE LENGTH	5,000	5,000	5,000	10,000	10,000	
E	APPROACH SLOPE	20:1	20:1	20:1	34:1	34:1	

A - UTILITY RUNWAYS
B - RUNWAYS LARGER THAN UTILITY
C - VISIBILITY MINIMUMS GREATER THAN 3/4 MILE
D - VISIBILITY MINIMUMS AS LOW AS 3/4 MILE
E - PRECISION INSTRUMENT APPROACH SLOPE IS 50:1 FOR INNER 10,000 FEET AND 40:1 FOR AN ADDITIONAL 40,000 FEET

- NOTES:
- OBSTRUCTIONS SHOWN WITHIN OBSTRUCTION GRID AREA ARE OBJECTS WITH THE HIGHEST PENETRATION AMOUNT FOR THAT AREA.
 - TOTAL OBSTRUCTIONS = ## REFERS TO THE TOTAL NUMBER OF OBSTRUCTIONS WITHIN THE HATCHED OBSTRUCTION GRID AREA.
 - SEE SHEET 7 FOR OBSTRUCTION TABLES.
 - SEE INNER APPROACH PLAN AND PROFILE SHEETS FOR CLOSE-IN OBSTRUCTIONS. (SHOWN AS SYMBOL ONLY)
 - USGS QUADRANGLE BASE MAPS OBTAINED NOVEMBER, 2014.

LEGEND	
DESCRIPTION	SYMBOL
OBSTRUCTION	▲ 8000
OBSTRUCTION GRID AREA	

ZONING RESTRICTIONS	
SEE SAN MIGUEL COUNTY LAND USE CODE, ARTICLE 5-STANDARDS, SECTION 5-418 TELLURIDE REGIONAL AIRPORT	

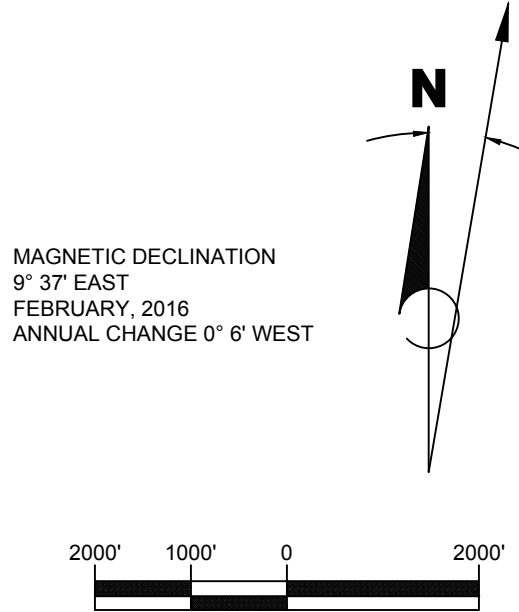

RS&H

RS&H, Inc.
4700 S. Syracuse Street, Suite 300
Denver, CO 80237
303-409-9700 FAX 303-409-9701
www.rsandh.com

TELLURIDE
REGIONAL AIRPORT

TELLURIDE
REGIONAL
AIRPORT
TELLURIDE, CO

AIRPORT
LAYOUT
PLAN

CONSULTANTS

REVISIONS

NO.	DESCRIPTION	DATE

DATE ISSUED: JUNE 2016

REVIEWED BY: DC / MLB

DRAWN BY: SD

DESIGNED BY: TJM

PROJECT NUMBER
224-3624-001

© 2016 RS&H, INC.

SHEET TITLE
FAR
PART 77
AIRSPACE
SURFACES
DRAWING

SHEET NUMBER

6 OF 13

DRAFT