

CURVE DATA

- C-1 R = 35.00', Δ = 90°00'00", L = 54.98'
CH - N 64°45'12" E, 49.50'
C-2 R = 50.00', Δ = 90°00'00", L = 78.54'
CH - N 64°45'12" E, 70.71'
C-3 R = 35.00', Δ = 90°00'00", L = 54.98'
CH - N 25°14'48" W, 49.50'
C-4 R = 50.00', Δ = 90°00'00", L = 78.54'
CH - N 25°14'48" W, 70.71'

Note: All bearings for this Plat were taken from existing monuments - south side of Colorado Highway 145.

220160
BACKMAN VILLAGE SUBD. AMENDED
TELLURIDE COMPANY
TO
WHOM IT MAY CONCERN
STATE OF COLORADO
COUNTY OF SAN MIGUEL
FILED FOR RECORD AT 10:10 AM
A. H. MARCH 10, 1981
AND ONLY RECORDED IN
BOOK PLAT # 1 PAGE 328
BY *Gay Capps* Recorder
FEE \$ 10.00
DUPY

BACKMAN VILLAGE
SUBDIVISION
AMENDED PLAT NO. 1

SCALE 1" = 50'
DRAWING # SBV - 1

TELLURIDE
SKI AREA
PLANNING AND
DESIGN DEPT.
TELLURIDE COMPANY INC.
P.O. BOX 307, TELLURIDE, CO. 81435
(303) 728 3856

NOTES

CERTIFICATE OF OWNERSHIP - THE TELLURIDE COMPANY

KNOW ALL PERSONS BY THESE PRESENTS:
That The Telluride Company, a Colorado Corporation, is the owner in fee simple of all the property described below. And, has by these presents laid out, platted and subdivided the same into lots as shown hereon including streets and easements shown hereon for access and utility purposes:

Beginning at Corner No. 10 of the Dakota Placer; THENCE N 10°15'00" E, 212.02'; THENCE N 70°11'24" W, 634.93'; THENCE S 10°00'00" W, 697.50'; THENCE S 75°05'21" E, 259.79'; THENCE N 70°00'00" E, 224.01'; THENCE N 19°45'12" E, 13.01'; THENCE N 68°51'42" E, 129.23'; THENCE N 79°00'00" E, 138.47'; THENCE N 59°00'00" E, 163.48'; THENCE N 65°15'00" W, 200.23'. To the point of beginning containing 9.0116 acres, more or less.

Executed this 6th day of MARCH, A.D., 1981.
By: *Donald D. O'Brien* Executive Officer Attest: *Gay Capps*

CERTIFICATE OF DEDICATION - THE TELLURIDE COMPANY

KNOW ALL PERSONS BY THESE PRESENTS:
That The Telluride Company, a Colorado Corporation, dedicates to the Town of Telluride the property described below according to the Plat and subdivision as set forth hereon:

- A. A Portion of Mahoney Drive - Beginning at Corner No. 10 of the Dakota Placer (MS2238); THENCE N 10°15'00" E, 39.39'. To the true point of beginning. THENCE N 10°15'00" E, 172.63'; THENCE N 70°11'24" W, 2.96'; THENCE S 19°45'12" W, 169.29'; THENCE S 68°28'07" E, 33.48'. To the true point of beginning, containing 0.067 acres, more or less.

B. Fire Lane and Pedestrian Easement Right-of-Way
Executed this 6th day of MARCH, A.D., 1981.
By: *Donald D. O'Brien* Executive Officer Attest: *Gay Capps*

CERTIFICATE OF OWNERSHIP - SIMONIUS, VISCHER AND COMPANY

KNOW ALL PERSONS BY THESE PRESENTS:
That Simonius, Vischer and Company, a Swiss Limited Partnership, is the owner in fee simple of all the property described below. And, has by these presents laid out, platted and subdivided the same into lots as shown hereon including streets and easements shown hereon for access and utility purposes:

Beginning at Corner No. 10 of the Dakota Placer (MS2238); THENCE N 10°15'00" E, 220.82'; THENCE S 70°14'48" E, 474.10'; THENCE S 17°54'00" W, 106.69'; THENCE S 64°55'50" E, 82.68'; THENCE S 04°15'00" E, 170.00'; THENCE N 65°15'00" W, 595.00'. To the point of beginning, containing 2.888 acres, more or less.


Executed this 3rd day of MARCH, A.D., 1981.
By: *Simonius Vischer* Attorney in Fact Attest: *Gay Capps*

CERTIFICATE OF DEDICATION - SIMONIUS, VISCHER AND COMPANY

KNOW ALL PERSONS BY THESE PRESENTS:
That Simonius, Vischer and Company, a Swiss Limited Partnership, dedicates to the Town of Telluride the property described below according to the Plat and subdivision as set forth hereon:

- A. A Portion of Mahoney Drive - Beginning at Corner No. 10 of the Dakota Placer (MS2238); THENCE N 10°15'00" E, 39.39'. To the true point of beginning. THENCE N 10°15'00" E, 181.43'; THENCE S 70°14'48" E, 46.30'; THENCE S 19°45'12" W, 179.43'; THENCE N 68°28'07" W, 16.52'. To the true point of beginning, containing 0.129 acres, more or less.

B. River Park
Executed this 3rd day of MARCH, A.D., 1981.
By: *Simonius Vischer* Attorney in Fact Attest: *Gay Capps*

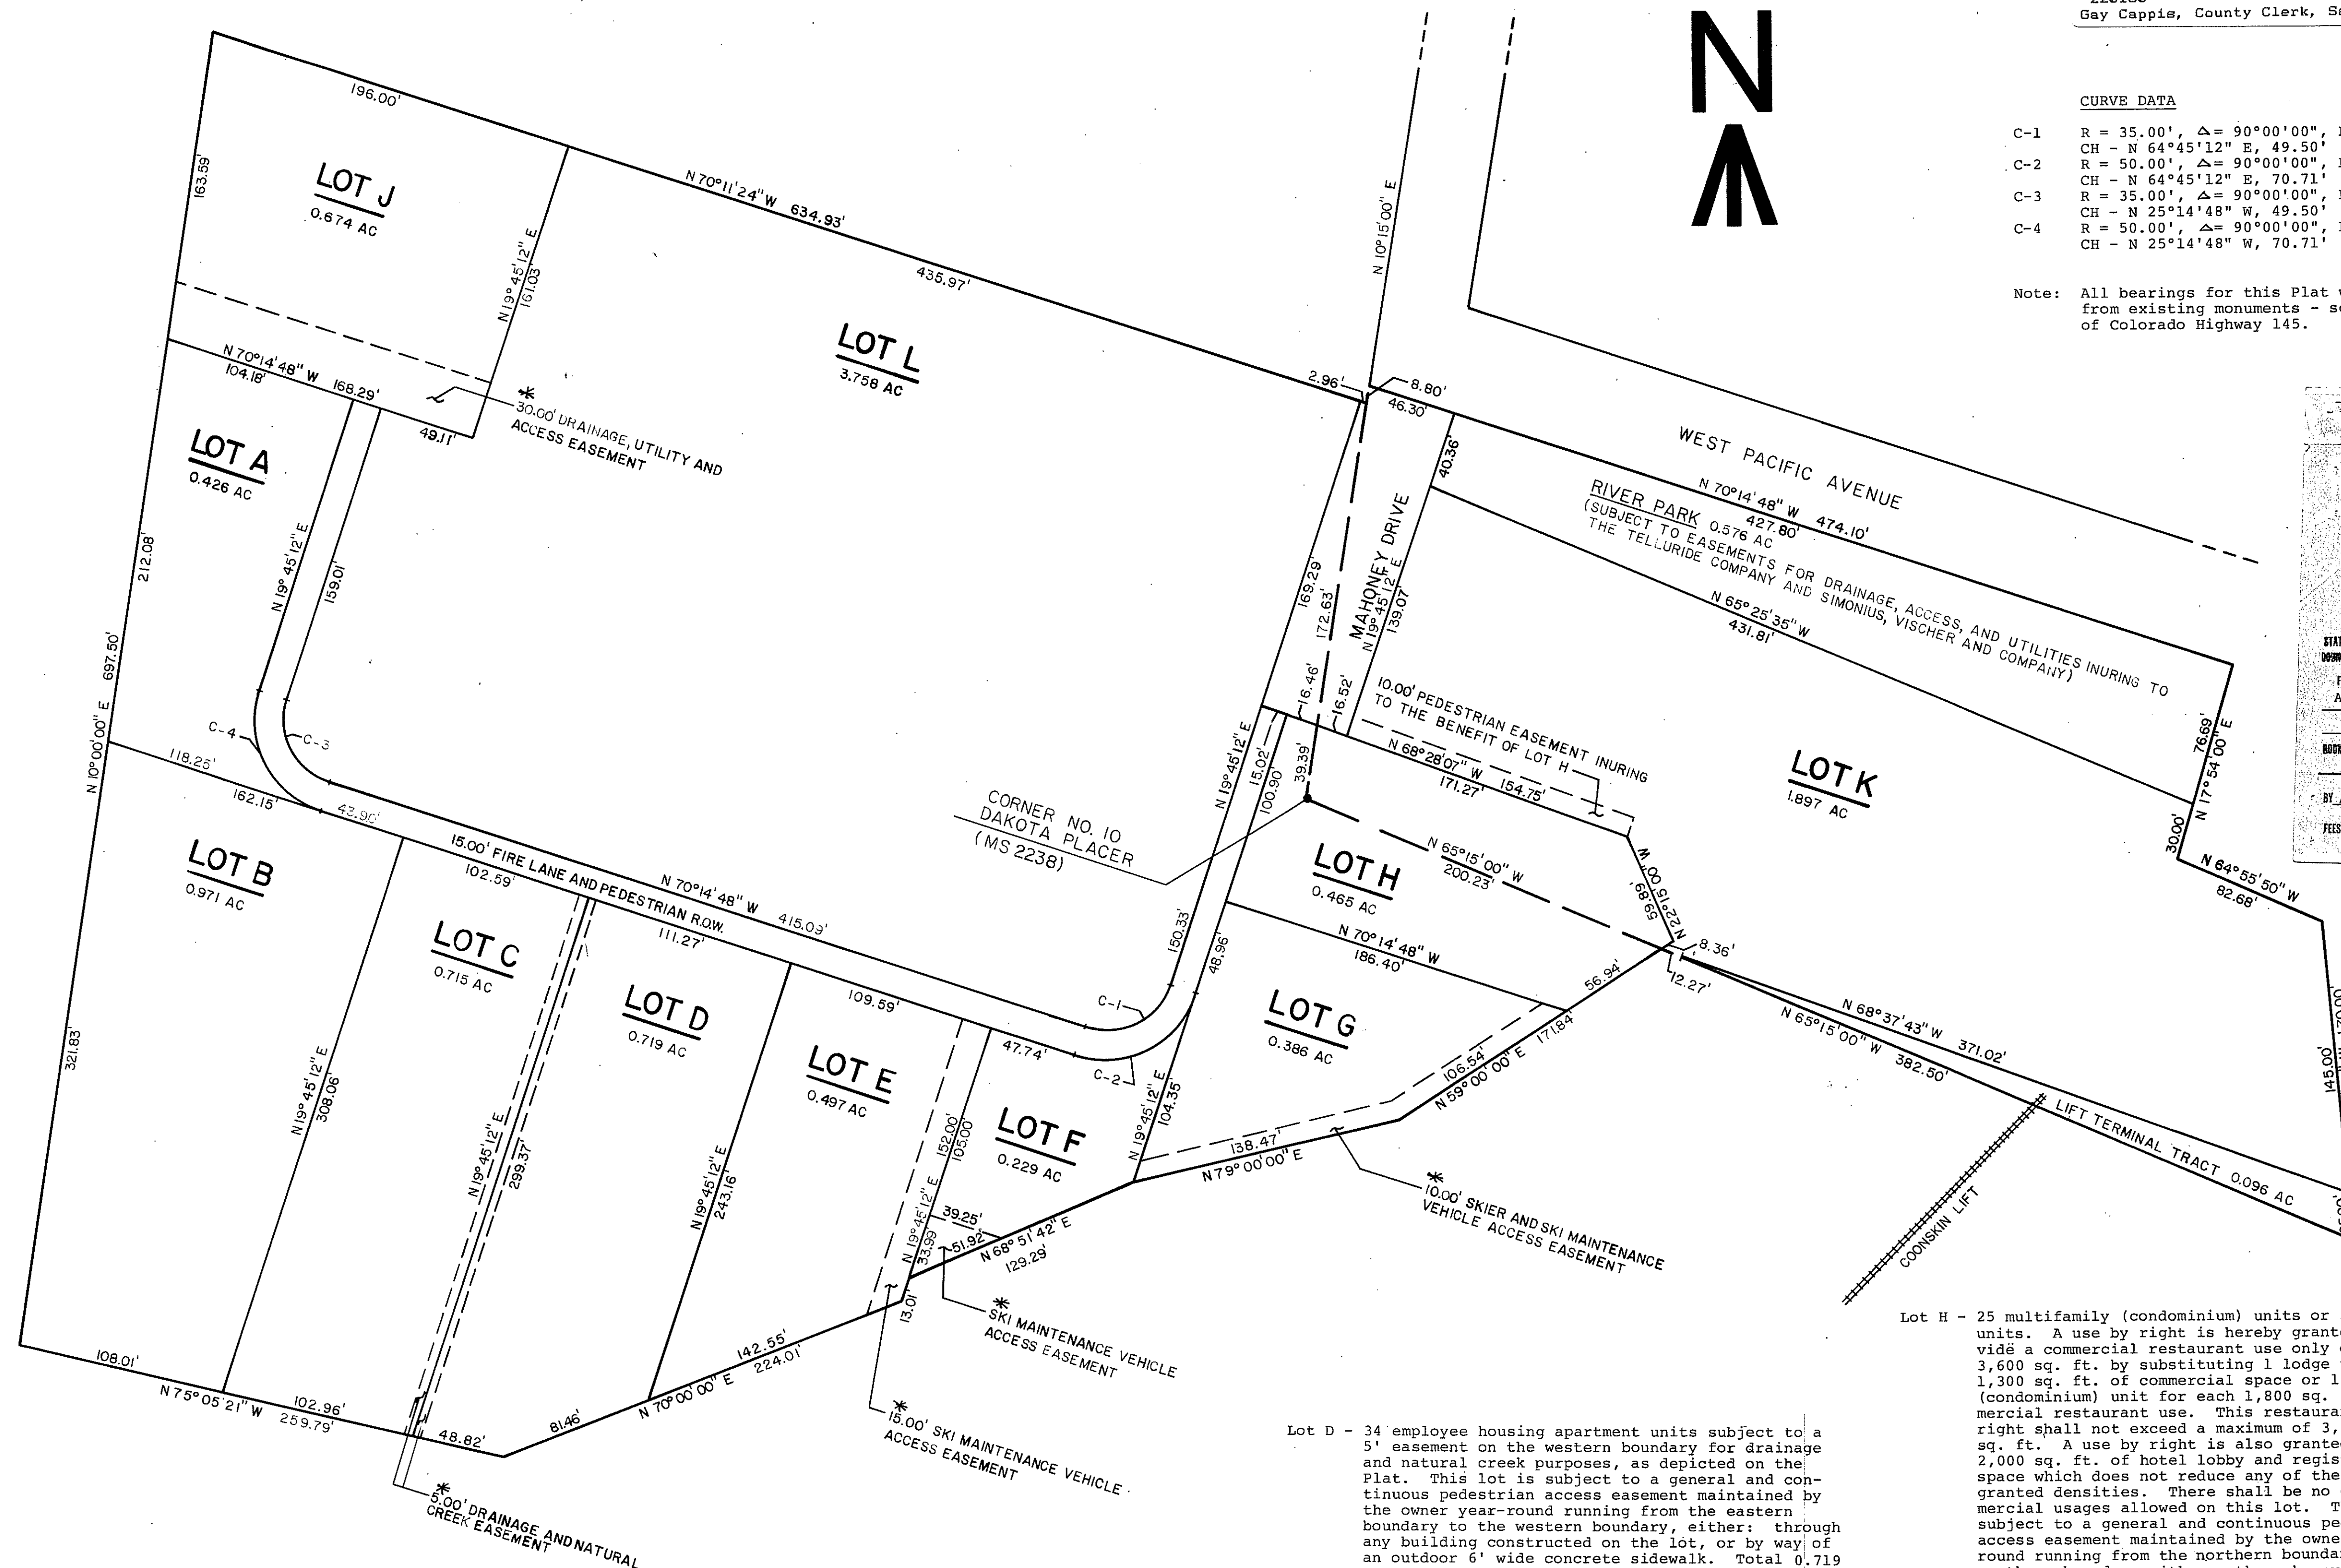

Town Council, Town of Telluride - Acceptance

The Town Council hereby approves and accepts on this 2nd day of February, 1981, this Backman Village Amended Plat No. 1, as set forth hereon, including associated utility plans, and roads appropriate for dedication to the Town of Telluride.

Attest: *Gay Capps* County Clerk Date: 2/16/81
By: *Donald D. O'Brien* Executive Officer

County Recorder's Certificate

Accepted for filing in the Office of the County Clerk and Recorder, San Miguel County, Colorado, on this 10th day of March, 1981. Reception Number 440160.
At Book Page 328
By: *Gay Capps* County Clerk Date: 3/14/81

Surveyor's Certificate

I, Roger D. Mahnke, do hereby certify that the foregoing instrument was prepared under my direct supervision in July, 1980, and accurately depicts a field survey of the same.

Roger D. Mahnke 6868 Colo. 6868

*Refers to easements which inure to the sole benefit of The Telluride Company.

This Plat is evolved from a generalized Site Coverage Plan, to insure integration and continuity of any improvements to be constructed hereon. Said Site Coverage Plan, as approved, is on file with the Telluride Historical and Architectural Review Commission, and shall be considered as a guideline in conjunction with the submission of building plans for any lot hereon.

LAND USES, DENSITIES AND EASEMENTS FOR LOTS

- Lot A - 36 employee housing apartment units. This lot is subject to a general and continuous pedestrian access easement maintained by the owner year-round running from the eastern boundary to the western boundary, either: through any building constructed on the lot, or by way of an outdoor 6' wide concrete sidewalk. Total 0.426 acres.
- Lot B - 34 employee housing apartment units. This lot is subject to a general and continuous pedestrian access easement maintained by the owner year-round running from the eastern boundary to the western boundary, either: through any building constructed on the lot, or by way of an outdoor 6' wide concrete sidewalk. Total 0.971 acres.
- Lot C - 34 employee housing apartment units subject to a 5' easement along the eastern boundary for drainage and natural creek purposes, as depicted on the Plat. This lot is subject to a general and continuous pedestrian access easement maintained by the owner year-round running from the eastern boundary to the western boundary, either: through any building constructed on the lot, or by way of an outdoor 6' wide concrete sidewalk. Total 0.715 acres.
- Lot D - 34 employee housing apartment units subject to a 5' easement on the western boundary for drainage and natural creek purposes, as depicted on the Plat. This lot is subject to a general and continuous pedestrian access easement maintained by the owner year-round running from the eastern boundary to the western boundary, either: through any building constructed on the lot, or by way of an outdoor 6' wide concrete sidewalk. Total 0.719 acres.
- Lot E - 32 employee housing apartment units. This lot is subject to a general and continuous pedestrian access easement maintained by the owner year-round running from the eastern boundary to the western boundary, either: through any building constructed on the lot, or by way of an outdoor 6' wide concrete sidewalk. Total 0.497 acres.
- Lot F - 13 multifamily (condominium) units or 19 lodging units; no right of commercial square footage substitution. This lot is subject to a general and continuous pedestrian access easement maintained by the owner year-round running from the eastern boundary to the western boundary, either: through any building constructed on the lot, or by way of an outdoor 6' wide concrete sidewalk. Total 0.229 acres.
- Lot G - 22 multifamily (condominium) units or 33 lodging units, a use by right is hereby granted to provide a commercial restaurant use only of up to 3,600 gross sq. ft. by substituting 1 lodge unit for 1,300 sq. ft. of commercial space or 1 multifamily (condominium) unit for each 1,800 sq. ft. of commercial restaurant use. This restaurant use by right shall not exceed a maximum of 3,600 sq. ft. A use by right is also granted for up to 2,000 sq. ft. of hotel lobby and registration desk space which does not reduce any of the above granted densities. There shall be no other commercial usages allowed on this lot. This lot is subject to a general and continuous pedestrian access easement maintained by the owner year-round running from the northern boundary south to a point where the western boundary of Lot G adjoins the eastern boundary of Lot F, either: through any building constructed on the lot, or by way of an outdoor 8' wide concrete sidewalk. Total 0.386 acres.

Lot H - 25 multifamily (condominium) units or 37 lodging units. A use by right is hereby granted to provide a commercial restaurant use only of up to 3,600 sq. ft. by substituting 1 lodge unit for 1,300 sq. ft. of commercial space or 1 multifamily (condominium) unit for each 1,800 sq. ft. of commercial restaurant use. This restaurant use by right shall not exceed a maximum of 3,600 gross sq. ft. A use by right is also granted for up to 2,000 sq. ft. of hotel lobby and registration desk space which does not reduce any of the above granted densities. There shall be no other commercial usages allowed on this lot. This lot is subject to a general and continuous pedestrian access easement maintained by the owner year-round running from the northern boundary to the southern boundary, either: through any building constructed on the lot, or by way of an outdoor 8' wide concrete sidewalk. Total 0.465 acres.

Lot I - 32 employee housing apartment units. This lot is subject to a general and continuous pedestrian access easement maintained by the owner year-round running from the eastern boundary to the western boundary, either: through any building constructed on the lot, or by way of an outdoor 6' wide concrete sidewalk. Total 0.386 acres.

Lot J - 13 multifamily (condominium) units or 19 lodging units; no right of commercial square footage substitution. This lot is subject to a general and continuous pedestrian access easement maintained by the owner year-round running from the eastern boundary to the western boundary, either: through any building constructed on the lot, or by way of an outdoor 6' wide concrete sidewalk. Total 0.674 acres.

Lot K - 22 multifamily (condominium) units or 33 lodging units, a use by right is hereby granted to provide a commercial restaurant use only of up to 3,600 gross sq. ft. by substituting 1 lodge unit for 1,300 sq. ft. of commercial space or 1 multifamily (condominium) unit for each 1,800 sq. ft. of commercial restaurant use. This restaurant use by right shall not exceed a maximum of 3,600 sq. ft. A use by right is also granted for up to 2,000 sq. ft. of hotel lobby and registration desk space which does not reduce any of the above granted densities. There shall be no other commercial usages allowed on this lot. This lot is subject to a general and continuous pedestrian access easement maintained by the owner year-round running from the northern boundary south to a point where the western boundary of Lot G adjoins the eastern boundary of Lot F, either: through any building constructed on the lot, or by way of an outdoor 8' wide concrete sidewalk. Total 1.897 acres.

Lot L - 25 multifamily (condominium) units or 37 lodging units. A use by right is hereby granted to provide a commercial restaurant use only of up to 3,600 sq. ft. by substituting 1 lodge unit for 1,300 sq. ft. of commercial space or 1 multifamily (condominium) unit for each 1,800 sq. ft. of commercial restaurant use. This restaurant use by right shall not exceed a maximum of 3,600 gross sq. ft. A use by right is also granted for up to 2,000 sq. ft. of hotel lobby and registration desk space which does not reduce any of the above granted densities. There shall be no other commercial usages allowed on this lot. This lot is subject to a general and continuous pedestrian access easement maintained by the owner year-round running from the northern boundary to the southern boundary, either: through any building constructed on the lot, or by way of an outdoor 8' wide concrete sidewalk. Total 3.758 acres.

Note: Commercial use rights on lots G and H are mutually transferrable when a common ownership assemblage exists.

Lot J - Parking. Total 0.674 acres.
Lot K - Base Facility. This improvement shall be used or dedicated to any use and purpose permitted within the current Commercial Zone (as of November 1, 1980), Town of Telluride, including but not limited to retail sales, businesses, restaurant and bar operations, office space, ski school, meeting rooms, emergency medical facilities, nursery and other such uses and activities associated with the operation of the ski area, to contain a maximum gross floor area of 25,000 square feet of commercial uses; this lot is also granted 40 multifamily (condominium) units or 60 lodging units with no substitution of uses for commercial square footage. This is subject to easements for pedestrian access and emergency access as The Telluride Company may deem necessary in the furtherance of the general operation of its Base Facility and the ski area in general. Total 1.897 acres.
Lot L - Parking. This lot fulfills cumulative off street parking requirements created by improvements on Lots A,B,C,D,E,F,G,H,J, and K as well as the Coonskin Lift, a proposed future lift, and the joint use of the parking lot by The Telluride Company and the Town of Telluride. Lot L is subject to a generalized access easement, guaranteeing access to all adjacent lots nonspecifically, pursuant to parking lot utilization plans and adjusted to actual use. Total 3.758 acres.